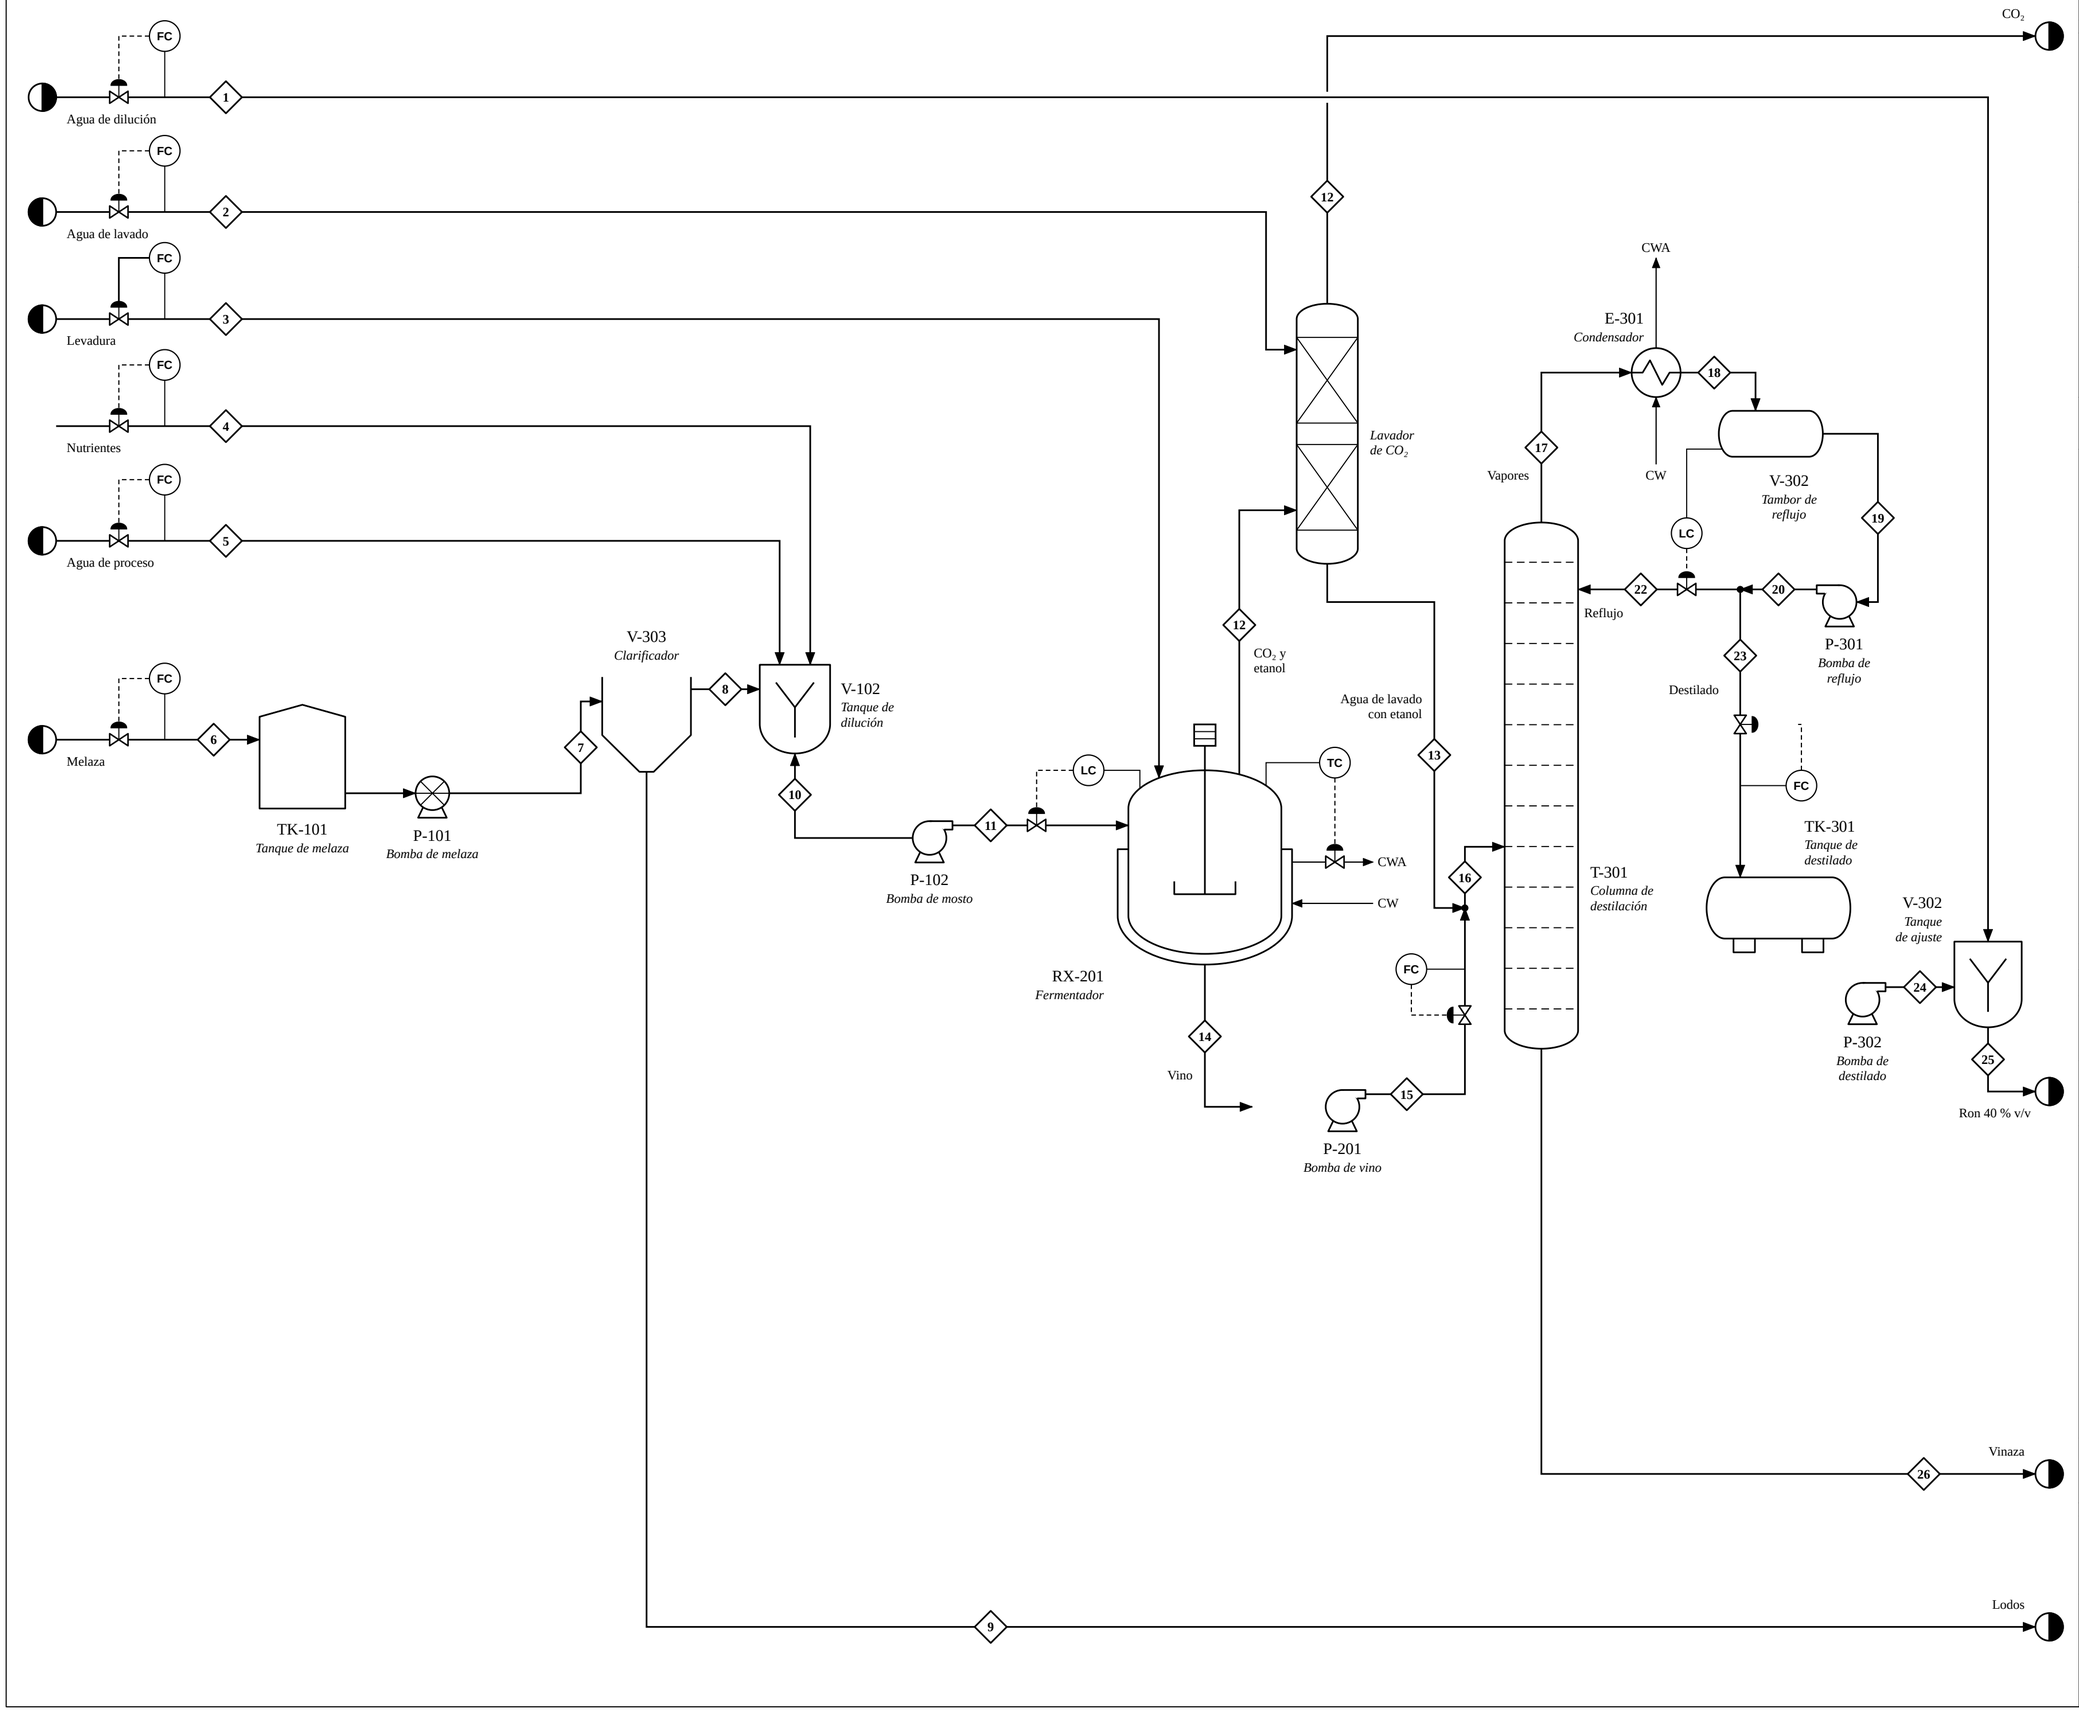


General Notes

Process Flow Diagram:
Production of Rum from Sugarcane Molasses

Servicios: CW (agua de enfriamiento), CWA (retorno de agua de enfriamiento).

Reactions

Hidrólisis de la sacarosa

$$C_{12}H_{22}O_{11} + H_2O \xrightarrow{\text{invertasa}} 2\ C_6H_{12}O_6$$

Fermentación alcohólica

$$C_6H_{12}O_6 \xrightarrow{\text{levadura}} 2\ C_2H_5OH + 2\ CO_2$$

Conventions

- Entrada o salida del proceso
- 1 — Número de corriente
- Recipiente horizontal
- Tanque de almacenamiento
- Columna de platos
- Columna empacada
- Fermentador agitado con camisa
- Tanque de mezcla
- Clarificador
- Bomba centrífuga
- Bomba de desplazamiento positivo
- Intercambiador de calor
- Válvula de control
- FC — Control de flujo
- LC — Control de nivel
- TC — Control de temperatura
- Señal de control
- Línea de servicio

Rev.	Date	Description	Checked
0	23/10/2026	Issued for comments	

Universidad de los Andes

Chemical Engineering Department

Drawn by:

Names	Codes

Approved by:

Process Flow Diagram:
Production of Rum from Sugarcane Molasses

Course:	Date:	Scale:
Unitary Operations	23/10/2026	None

Drawing Number	REV.
01	1